



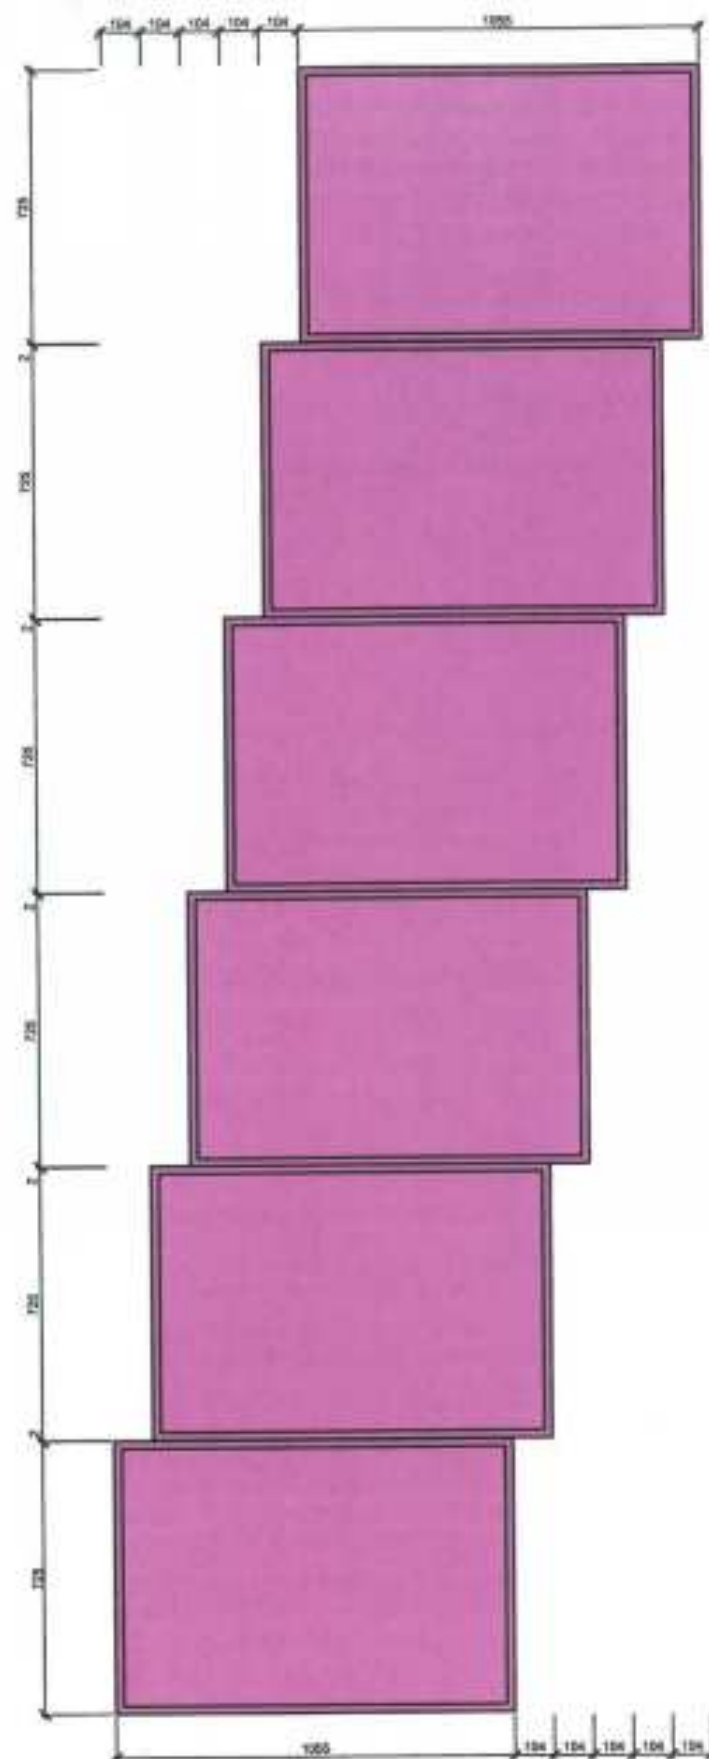


Sous-sol 6 x 76.48 = 458.88 m²

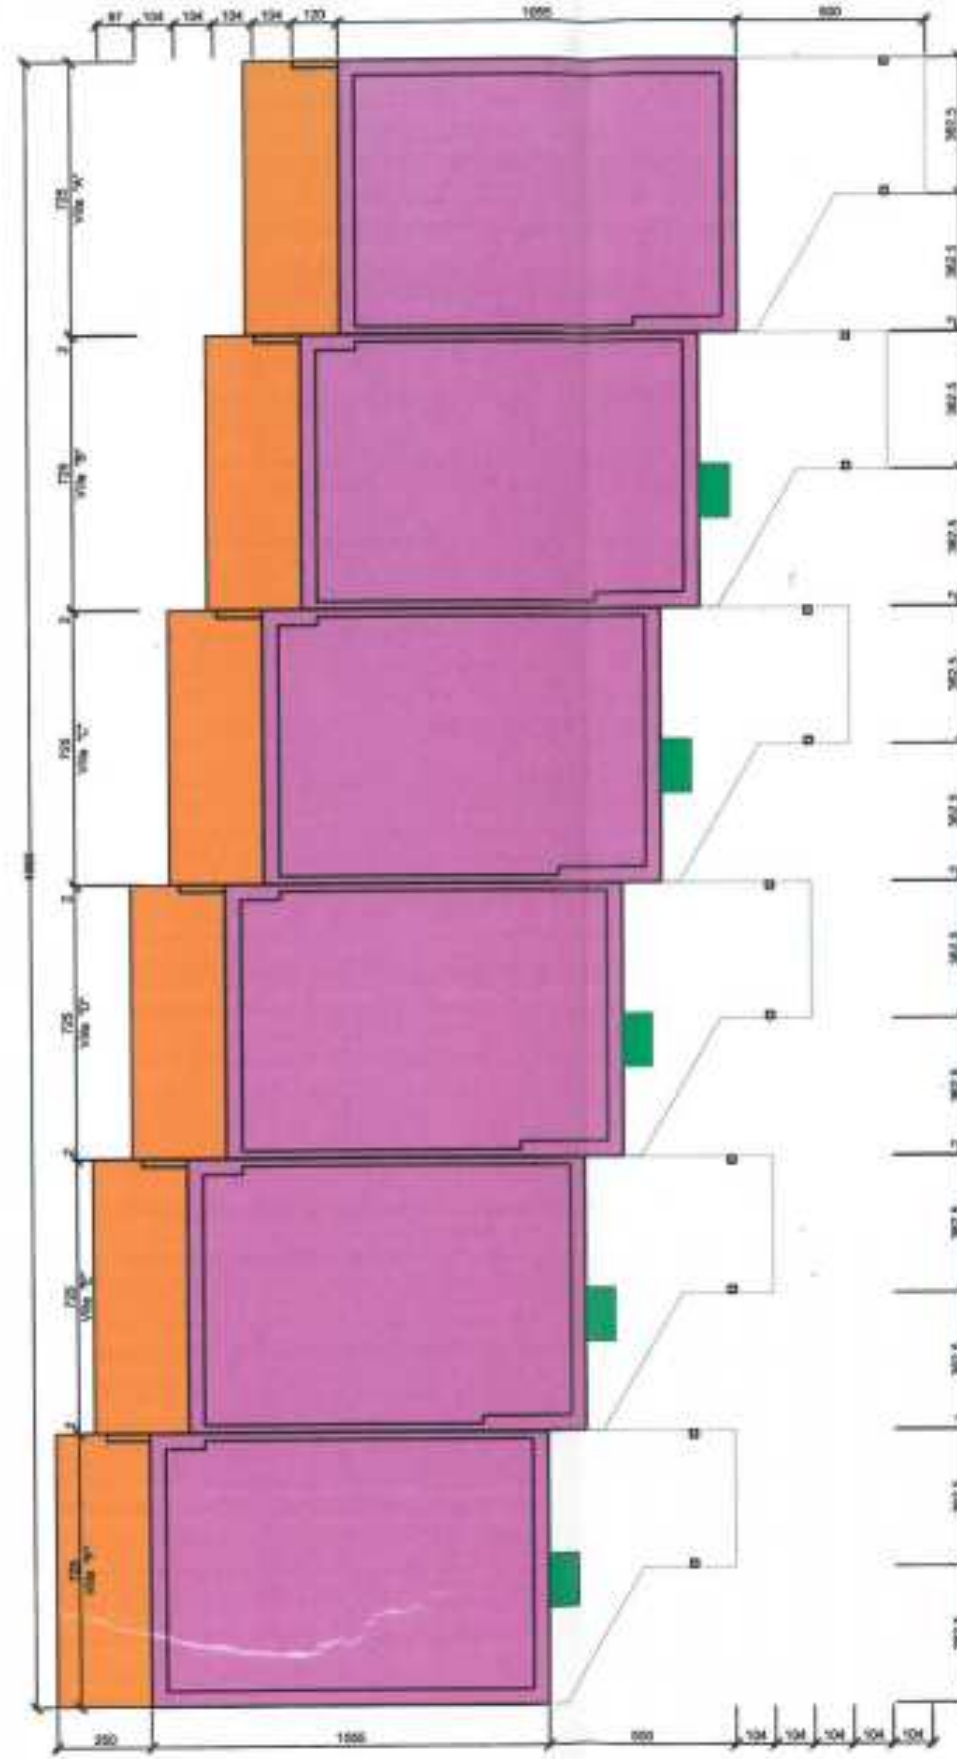

Rez de chaussée
Palier entrée
Terrasse

6 x 76.48 = 458.88 m²
5 x 1.12 = 5.60 m²
6 x 18.12 = 108.72 m²

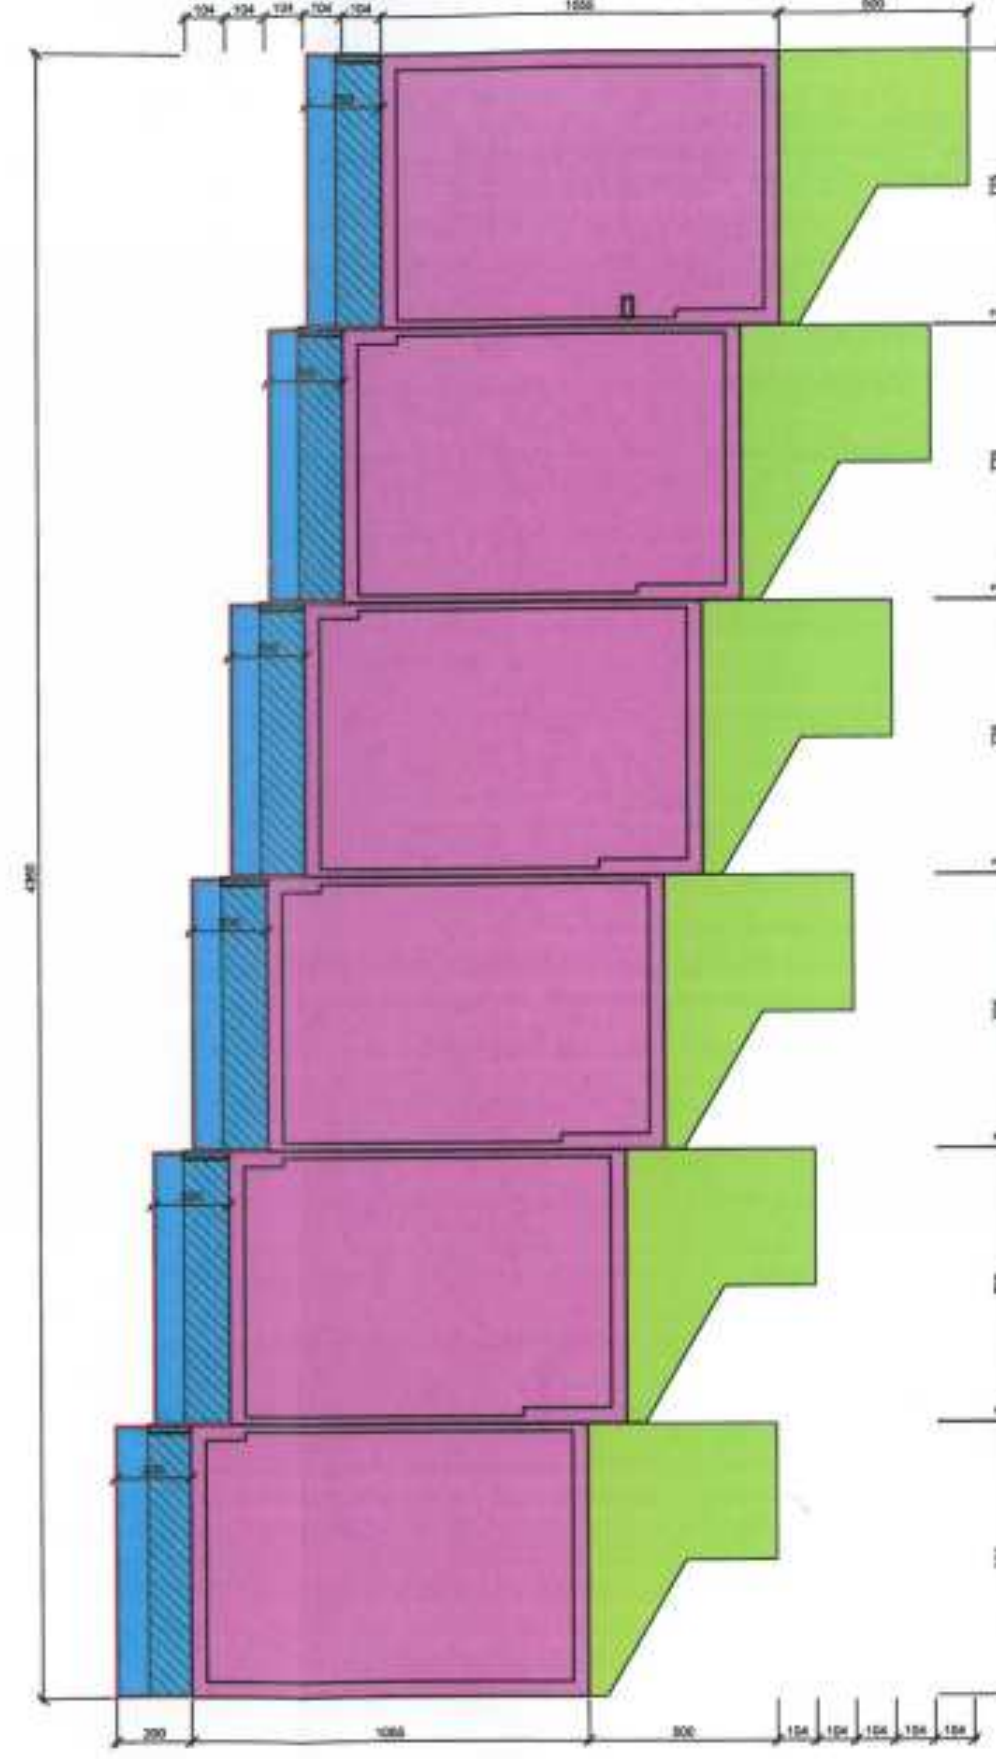

Etage
Balcon
Barrière balcon
Couvert balcon
Couvert entrée

6 x 76.48 = 458.88 m²
6 x 14.50 = 87.00 m²
6 x 10.05 = 60.30 m²
6 x 8.21 = 49.26 m²
6 x 23.74 = 142.44 m²

Calcul cube SIA
416

SOVALCO
Architecture & Construction


entreprise de construction générale
Tél. +4127 323 21 56
www.sovalco.ch info@sovalco.ch

CONSTRUCTION DE 6 VILLAS JUMELLES

PROJET

Commune : UVRIER
Parcelle : 7819
Echelle : 1:200

DESSIN : cb
DATE D. : 29.07.2019
MODIF. :

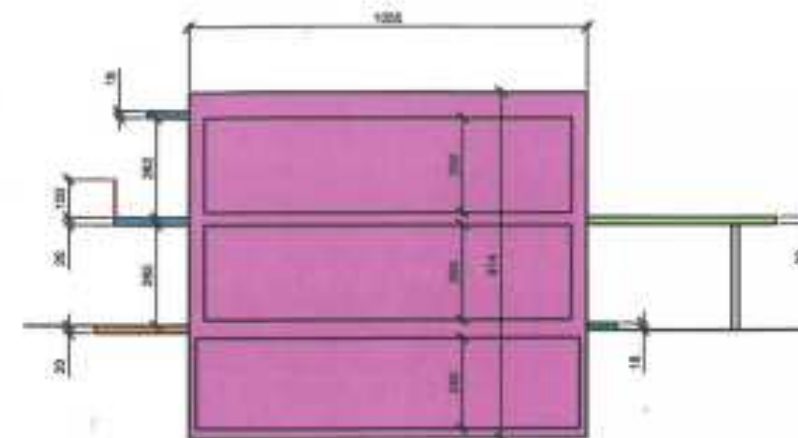

Bâtiment	458.88 x 9.14	= 4'194.63 m ³
Palier entrée	142.44 x 0.18	= 1.00 m ³
Terrasse	108.72 x 0.20	= 21.74 m ³
Couvert d'entrée	142.44 x 0.20	= 28.48 m ³
Balcon	87.00 x 0.20	= 17.40 m ³
Barrière balcon	10.05 x 1.00	= 10.05 m ³
Couvert balcon	49.26 x 0.18	= 8.86 m ³
TOTAL		= 4'282.16 m ³

Soit $4282.16 / 6 = 713.69$ m³ par villa

Calcul cube SIA
416

SOVALCO
Architecture & Construction


entreprise de construction générale
Tél. +4127 323 21 56
www.sovalco.ch info@sovalco.ch

CONSTRUCTION DE 6 VILLAS JUMELLES

PROJET

Commune : UVRIER
Parcelle : 7819
Echelle : 1-200

DESSIN : cb
DATE D. : 29.07.2019
MODIF. :

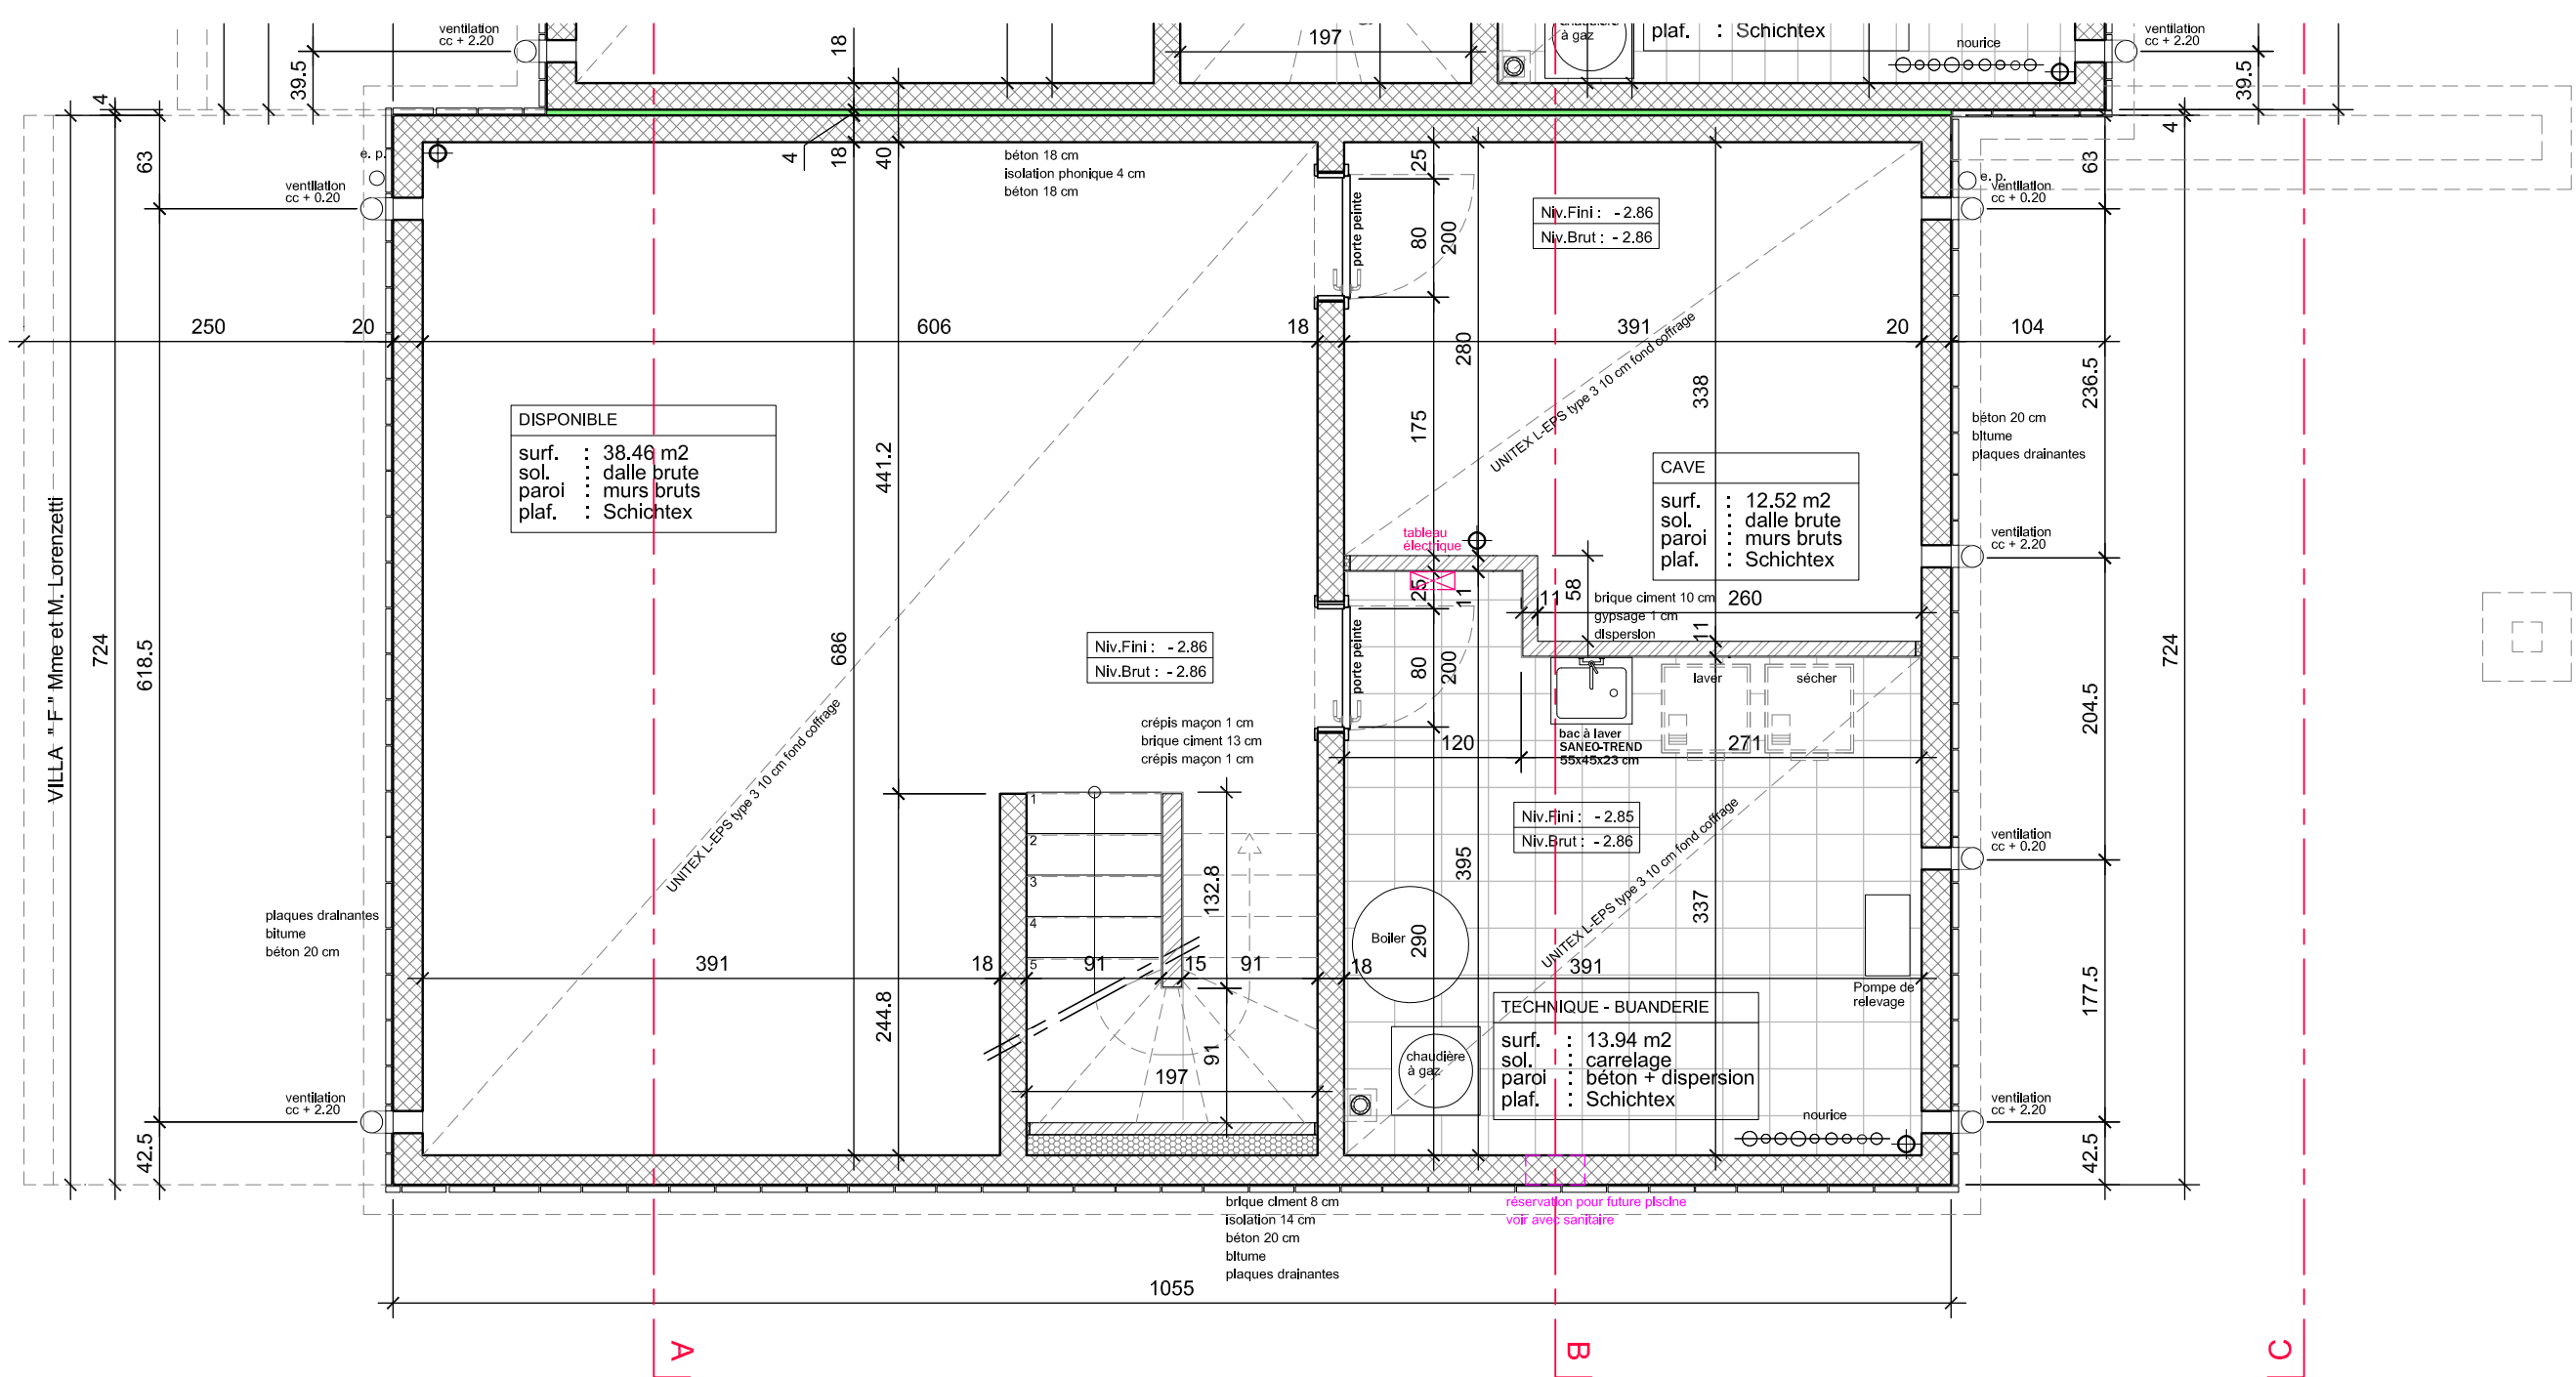

SOUS-SOL

Villa " F "

Mme. & M. LORENZETTI

"LACAPELA"

SOVALCO

Architecture & Construction

entreprise de construction générale

Tél. *4127 323 21 56

www.sovalco.ch

info@sovalco.ch

Commune : UVRIER

Parcelle : 7819

Echelle : 1-50

DESSIN : cb


DATE D. : 01.10.2019

MODIF. : 19.08.2020

L'entrepreneur est tenu de contrôler toutes les côtes et les niveaux sur les plans ainsi que sur le chantier.

Les murs et les ouvertures sont côtés finis

- Béton armé
- Brique ciment
- Plâtre
- Isolation
- Isolation phonique 4 cm
- Isolation ext. 14 cm
- Styrofoam 4 cm - tête de mur

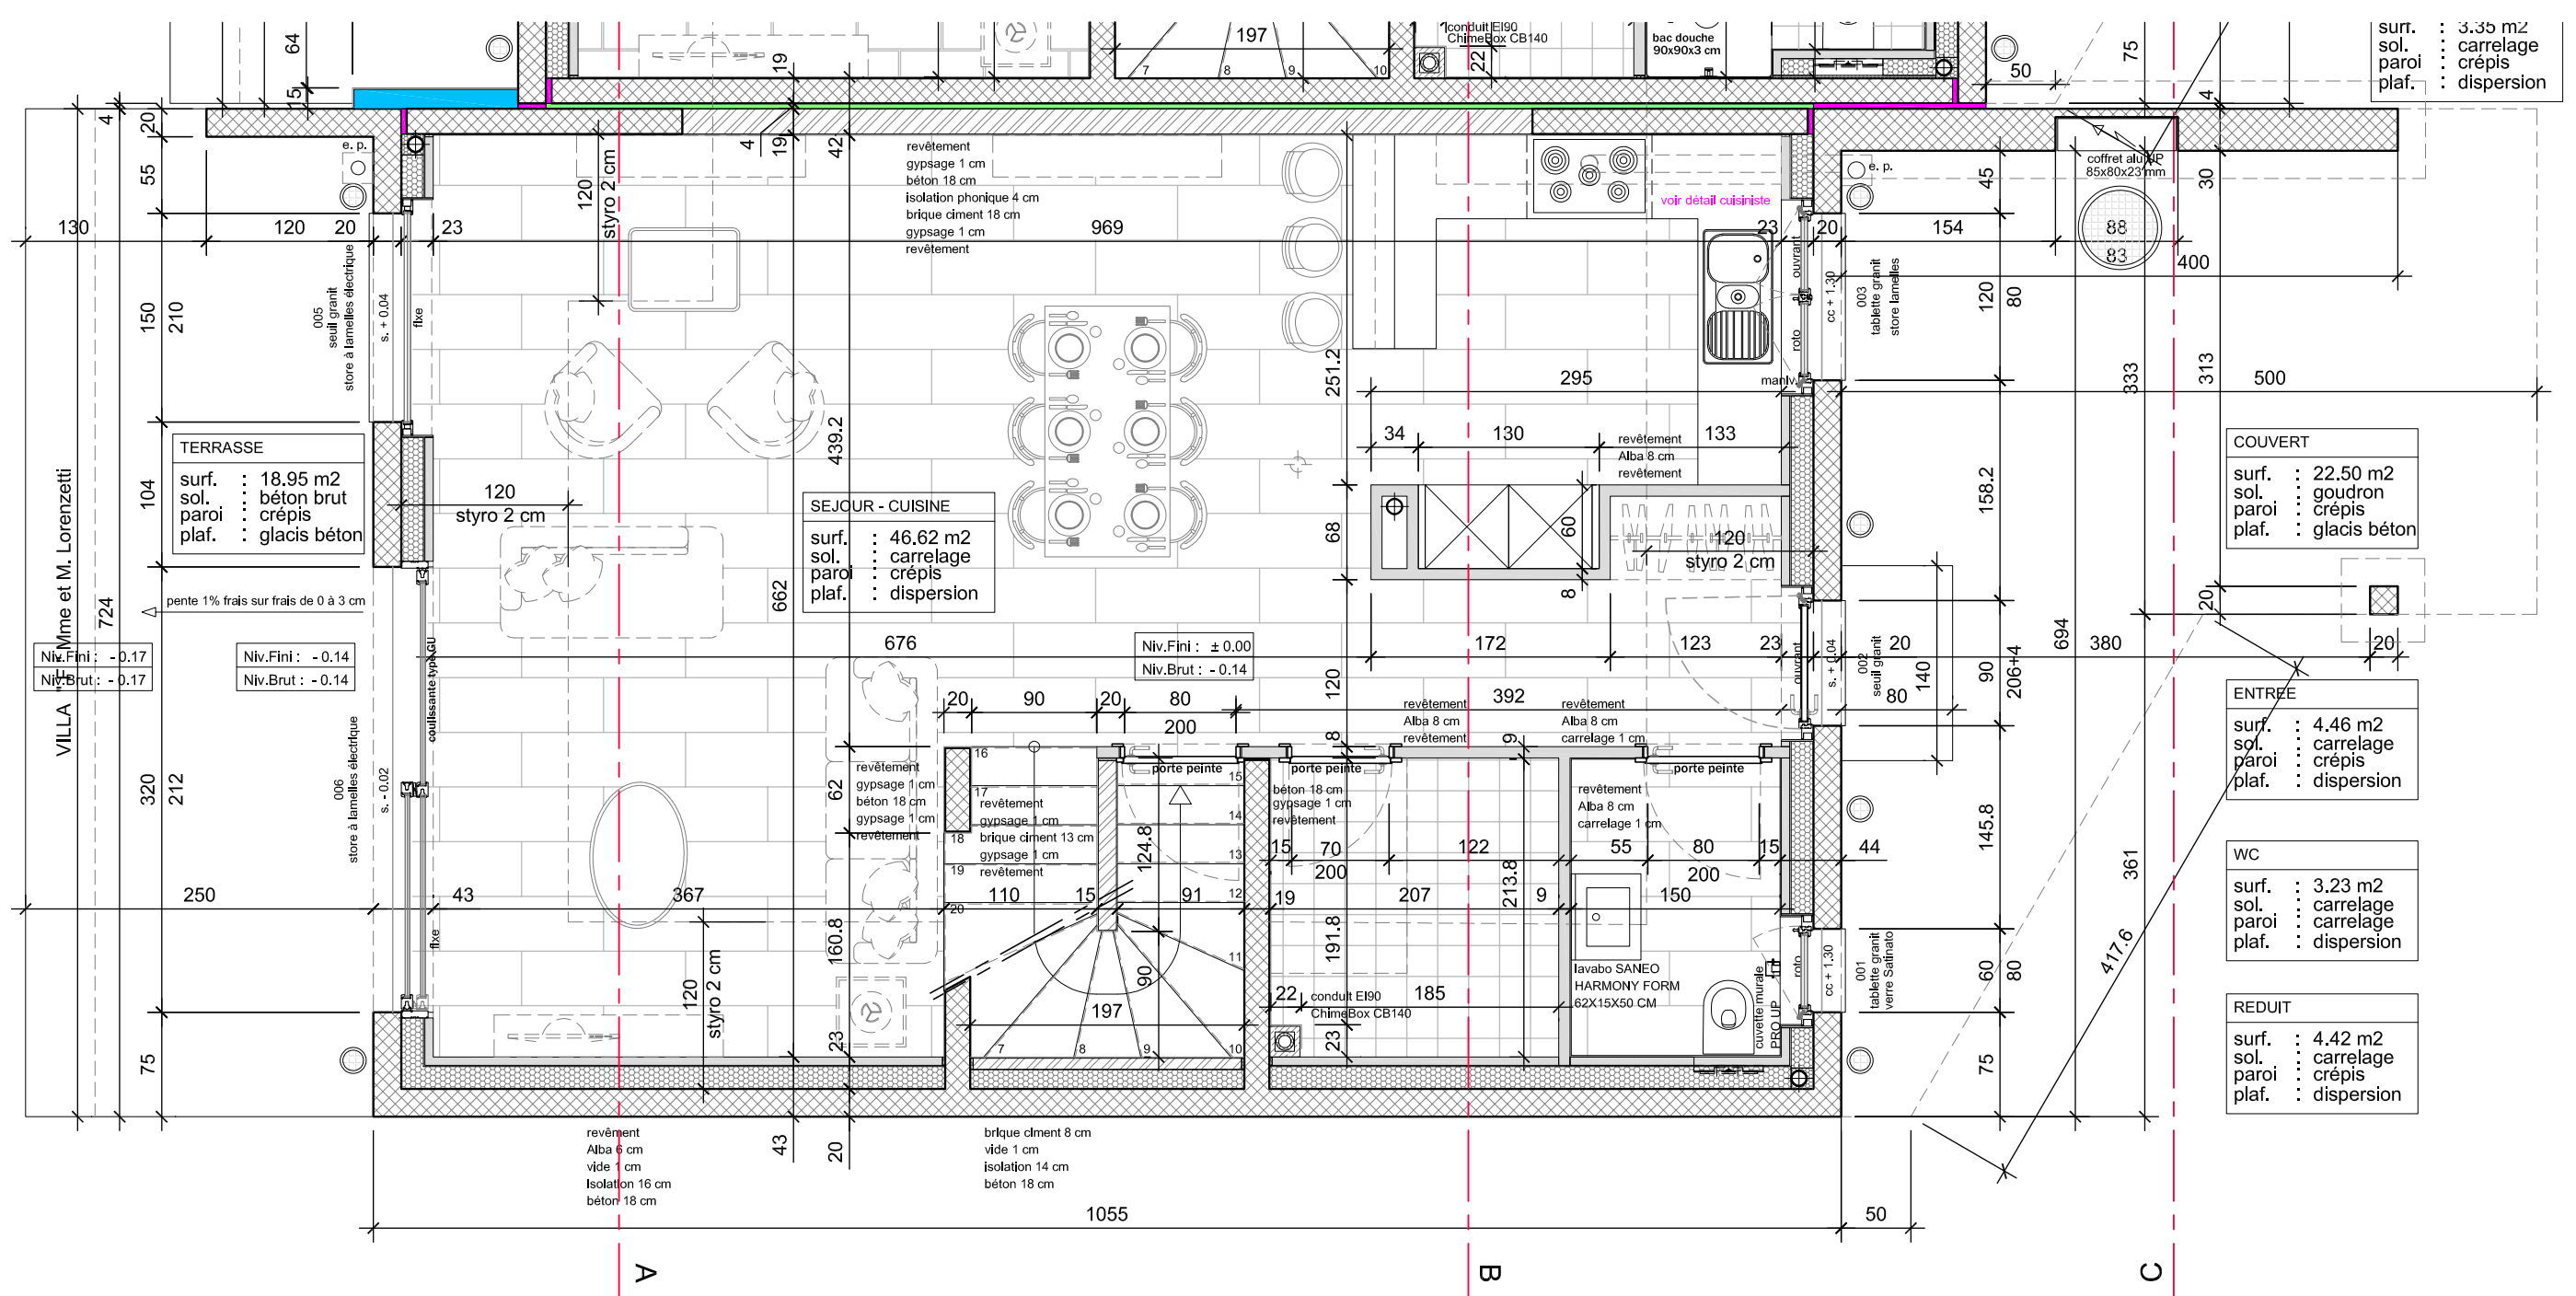

REZ DE CHAUSSEE

Villa " F "
Mme. & M. LORENZETTI
"LACAPELA"

L'entrepreneur est tenu de contrôler toutes les côtes et les niveaux sur les plans ainsi que sur le chantier.

Les murs et les ouvertures sont côtés finis

SOVALCO
 Architecture & Construction

entreprise de construction générale
 Tél. *4127 323 21 56
 www.sovalco.ch info@sovalco.ch


Commune : UVRIER
 Parcelle : 7819
 Echelle : 1-50

DESSIN : cb
 DATE D. : 01.10.2019
 MODIF. : 19.08.2020

DOUCHE	
surf.	: 5.61 m2
sol.	: carrelage
paroi	: carrelage
plaf.	: dispersion

DRESSING	
surf.	: 8.05 m2
sol.	: carrelage
paroi	: crépis
plaf.	: dispersion

CHAMBRE PARENTS	
surf.	: 10.85 m2
sol.	: carrelage
paroi	: crépis
plaf.	: dispersion

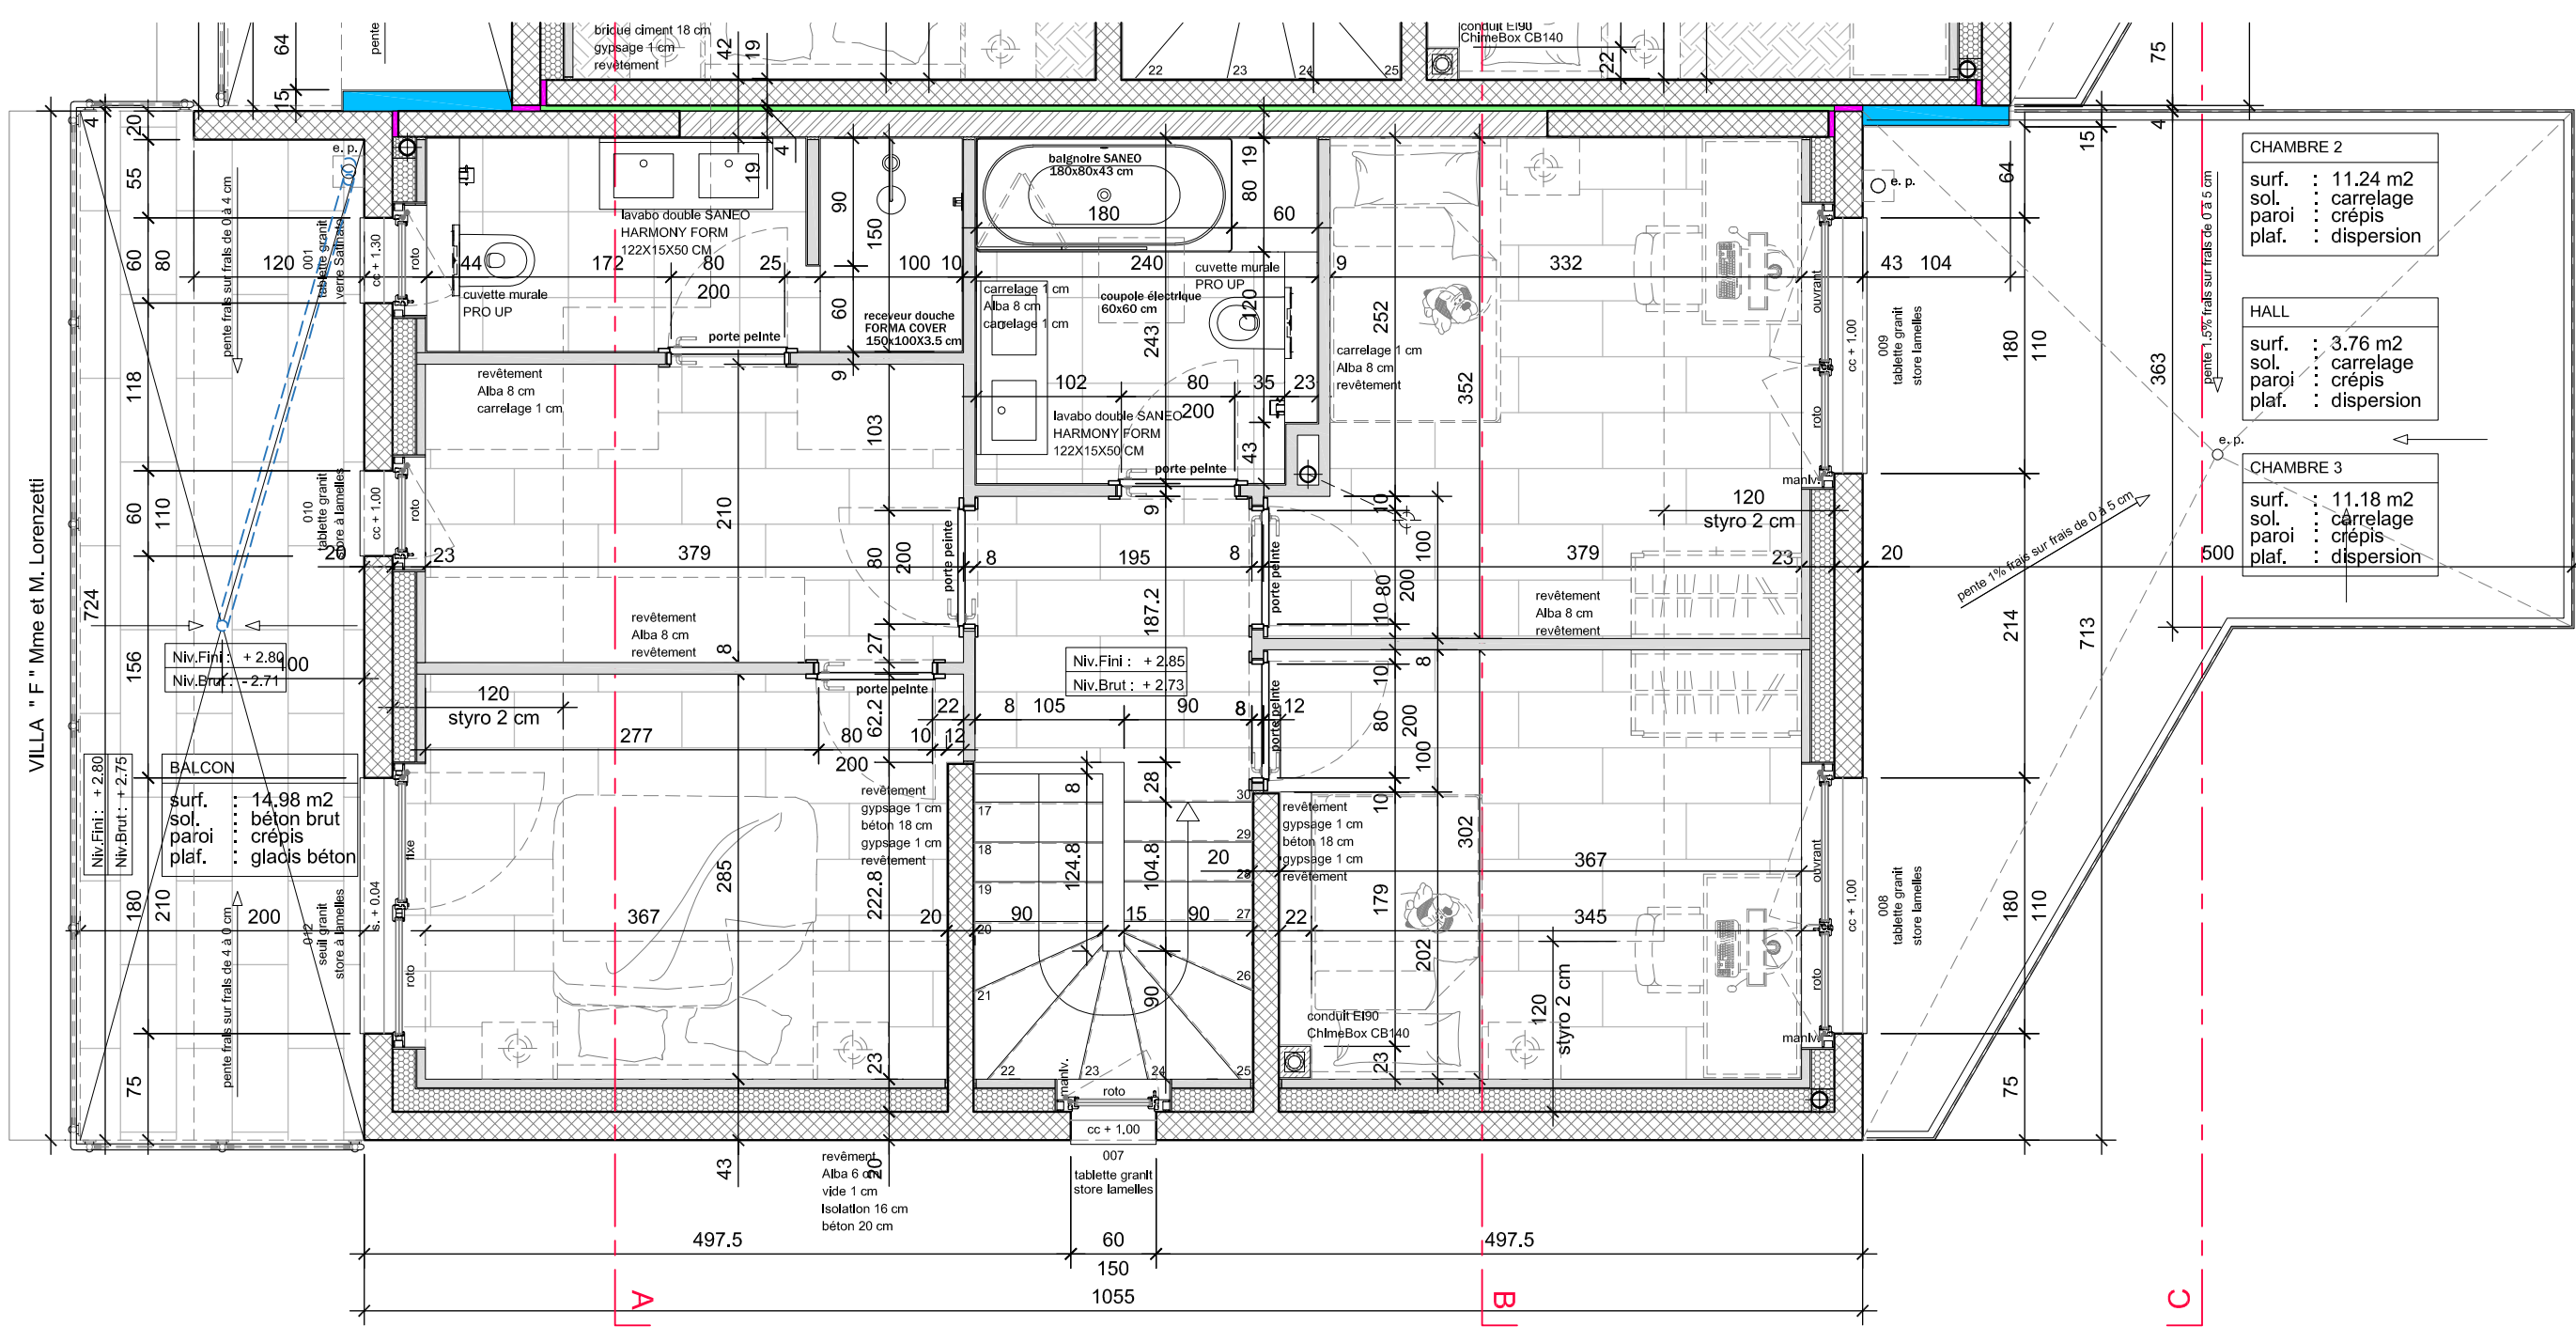

ETAGE

Villa " F "

Mme. & M. LORENZETTI

"LACAPELA"



entreprise de construction générale

Tél. *4127 323 21 56

www.sovalco.ch

info@sovalco.ch

Commune : UVRIER

Parcelle : 7819

Echelle : 1-50

DESSIN : cb


DATE D. : 01.10.2019

MODIF. : 19.08.2020

L'entrepreneur est tenu de contrôler toutes les côtes et les niveaux sur les plans ainsi que sur le chantier.

Les murs et les ouvertures sont côtés finis

- Béton armé
- Brique ciment
- Plâtre
- Isolation
- Isolation phonique 4 cm
- Isolation ext. 14 cm
- Styrofoam 4 cm - tête de mur

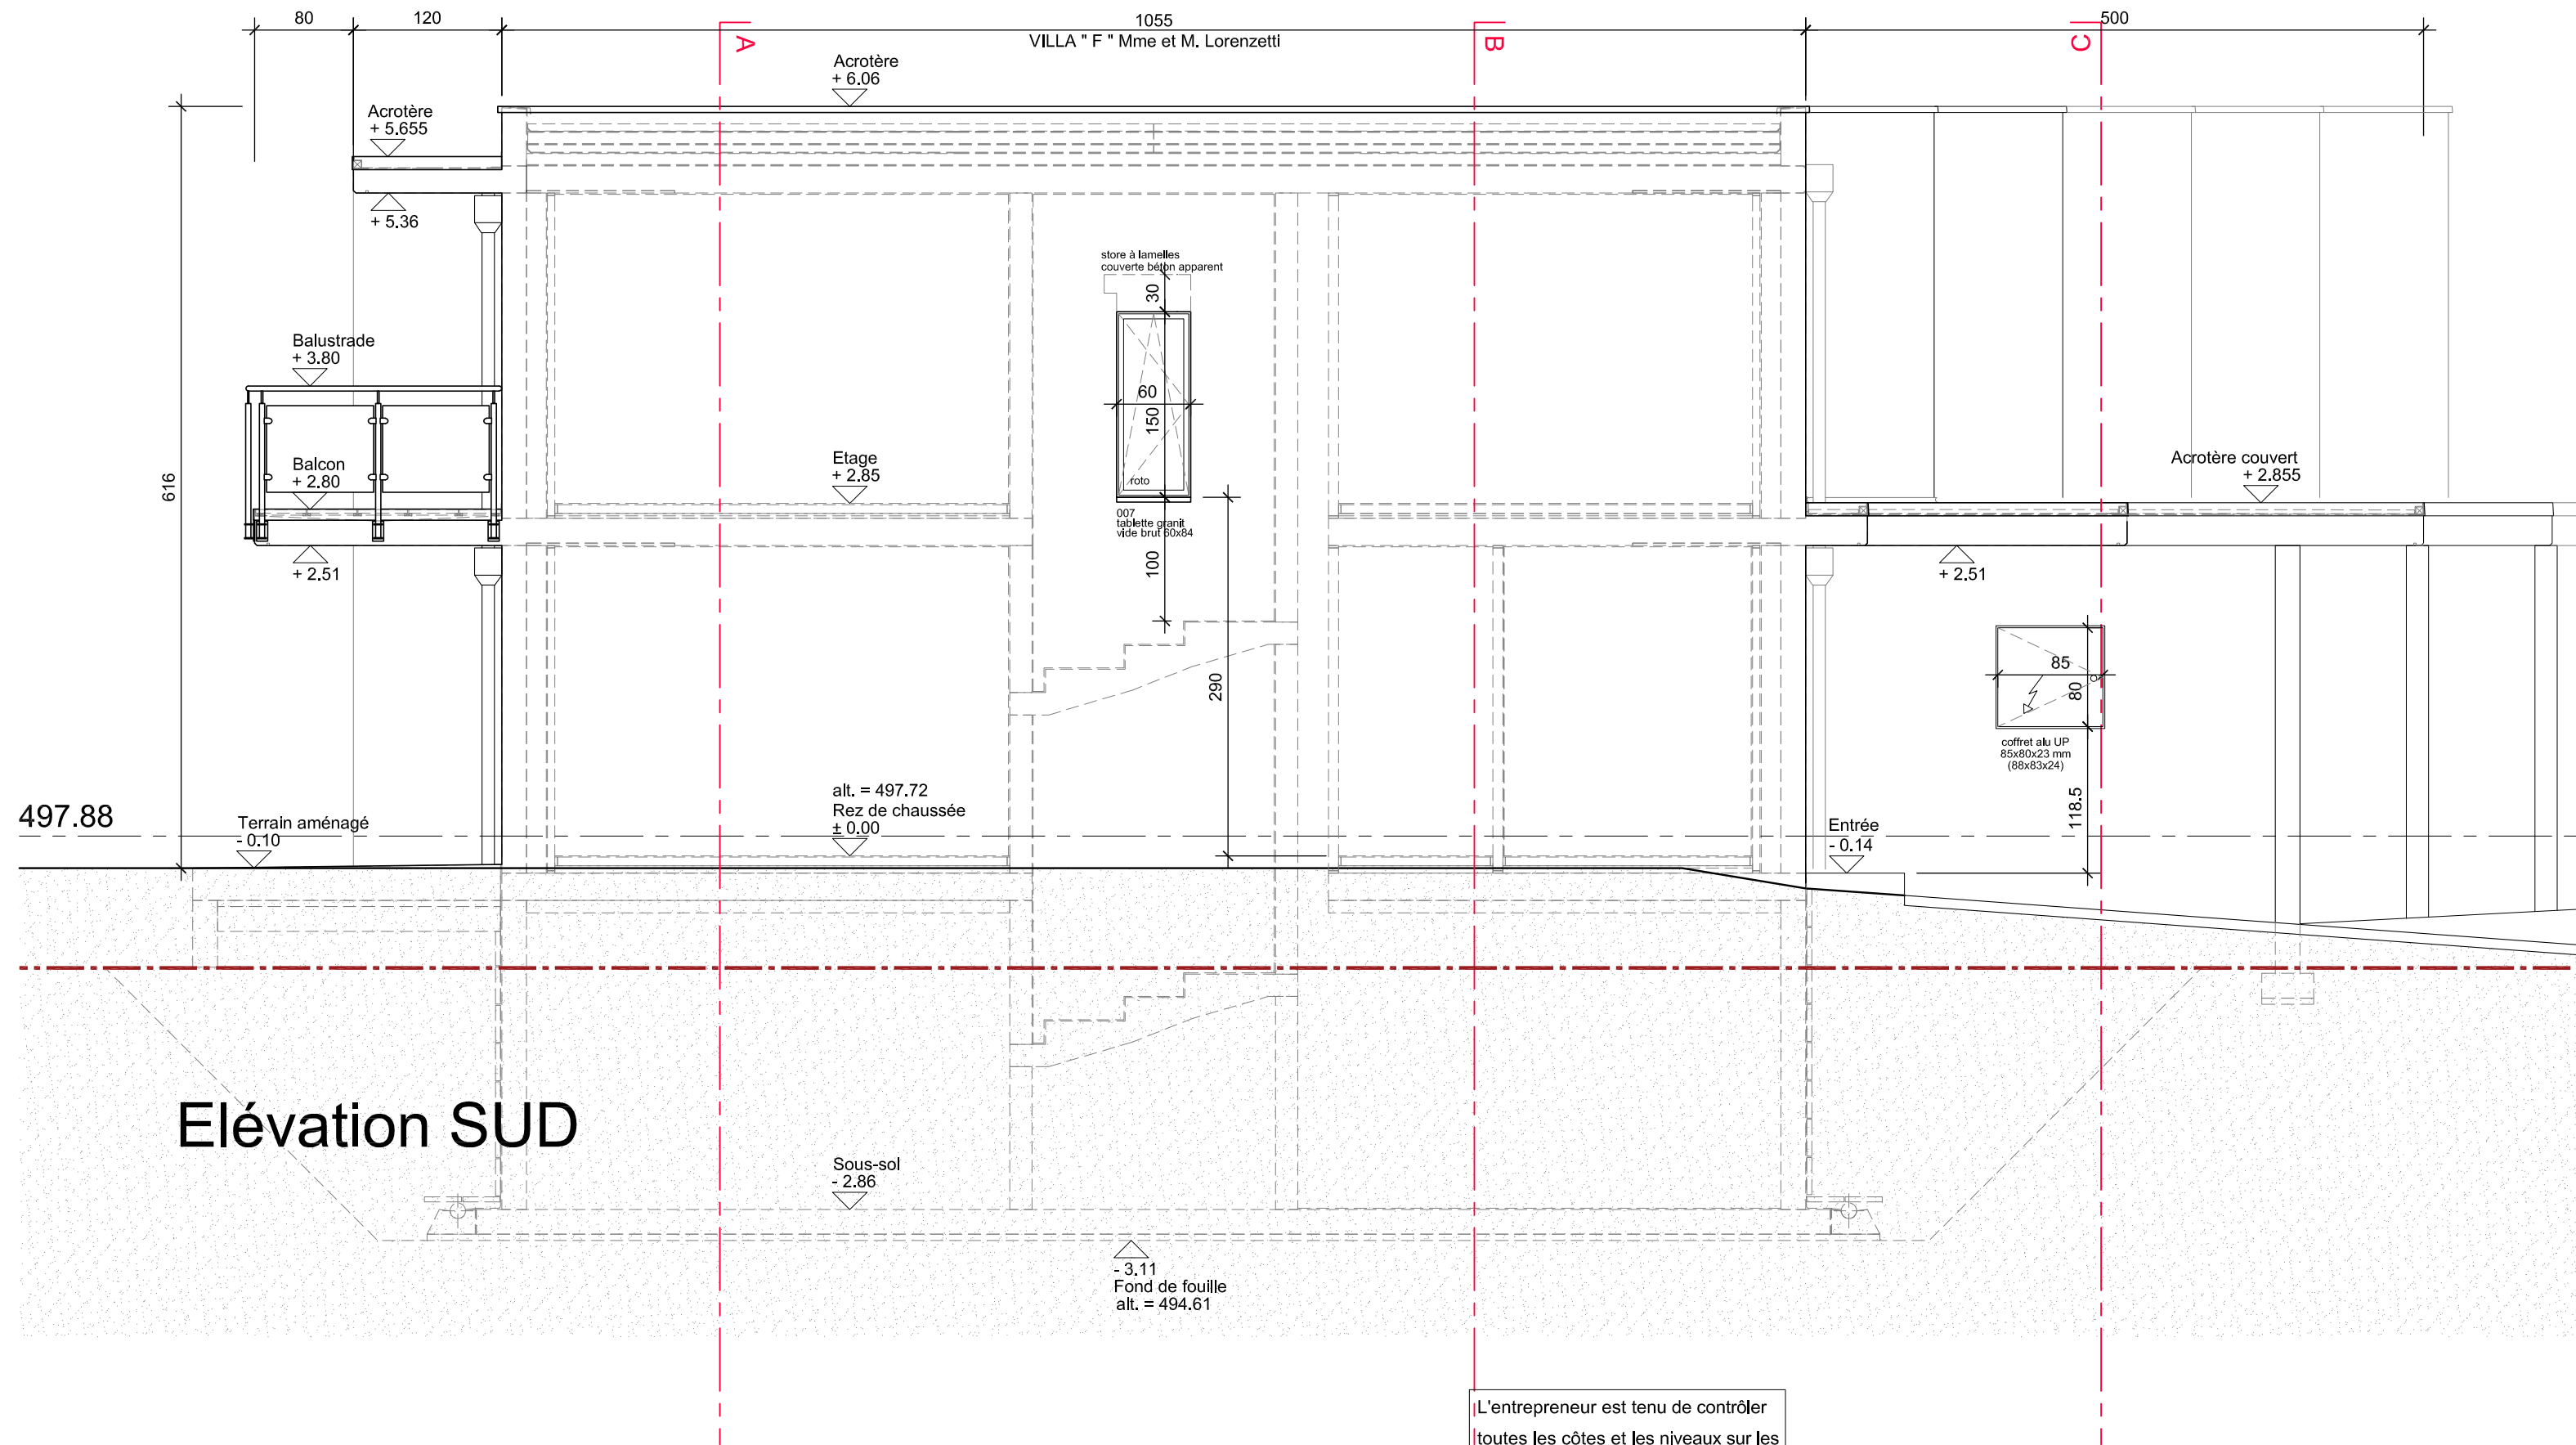

Elévation SUD

Villa " F "
Mme. & M. LORENZETTI
"LACAPELA"

L'entrepreneur est tenu de contrôler
toutes les côtes et les niveaux sur les
plans ainsi que sur le chantier.


Les murs et les ouvertures
sont côtés finis

SOVALCO
Architecture & Construction

entreprise de construction générale
Tél. *4127 323 21 56
www.sovalco.ch info@sovalco.ch

Commune : UVRIER
Parcelle : 7819
Echelle : 1-50

DESSIN : cb
DATE D. : 10.03.2020
MODIF. : 20.07.2020

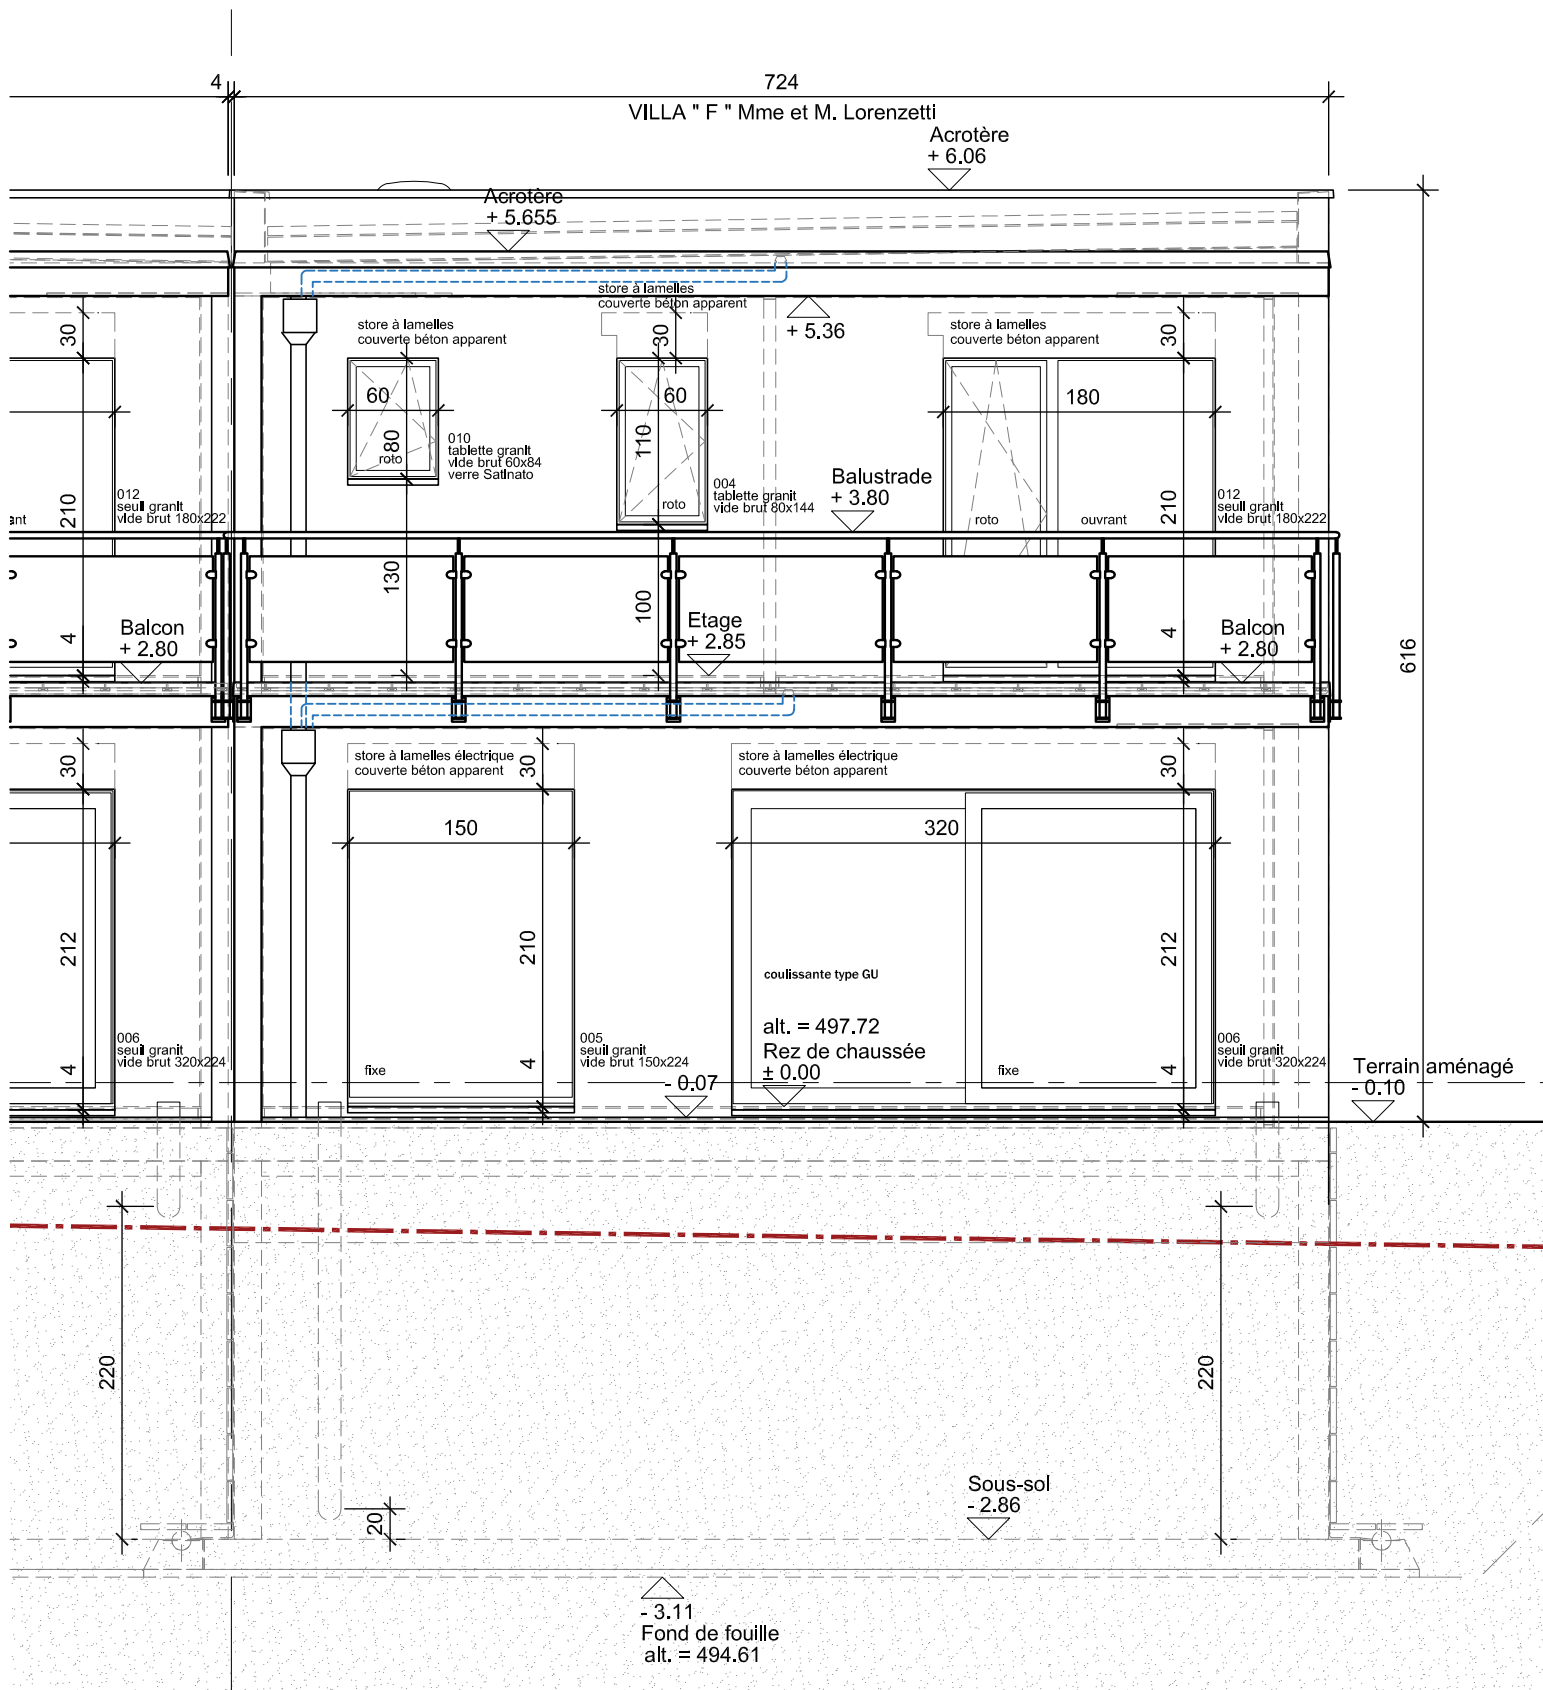

ELEVATION OUEST

Villa " F "

Mme. & M. LORENZETTI

"LACAPELA"

L'entrepreneur est tenu de contrôler toutes les côtes et les niveaux sur les plans ainsi que sur le chantier.


Les murs et les ouvertures sont côtés finis

SOVALCO
Architecture & Construction

entreprise de construction générale
Tél. *4127 323 21 56
www.ovalco.ch info@ovalco.ch

Commune : UVRIER
Parcelle : 7819
Echelle : 1-50

DESSIN : cb
DATE D. : 05.03.2020
MODIF. : 19.08.2020

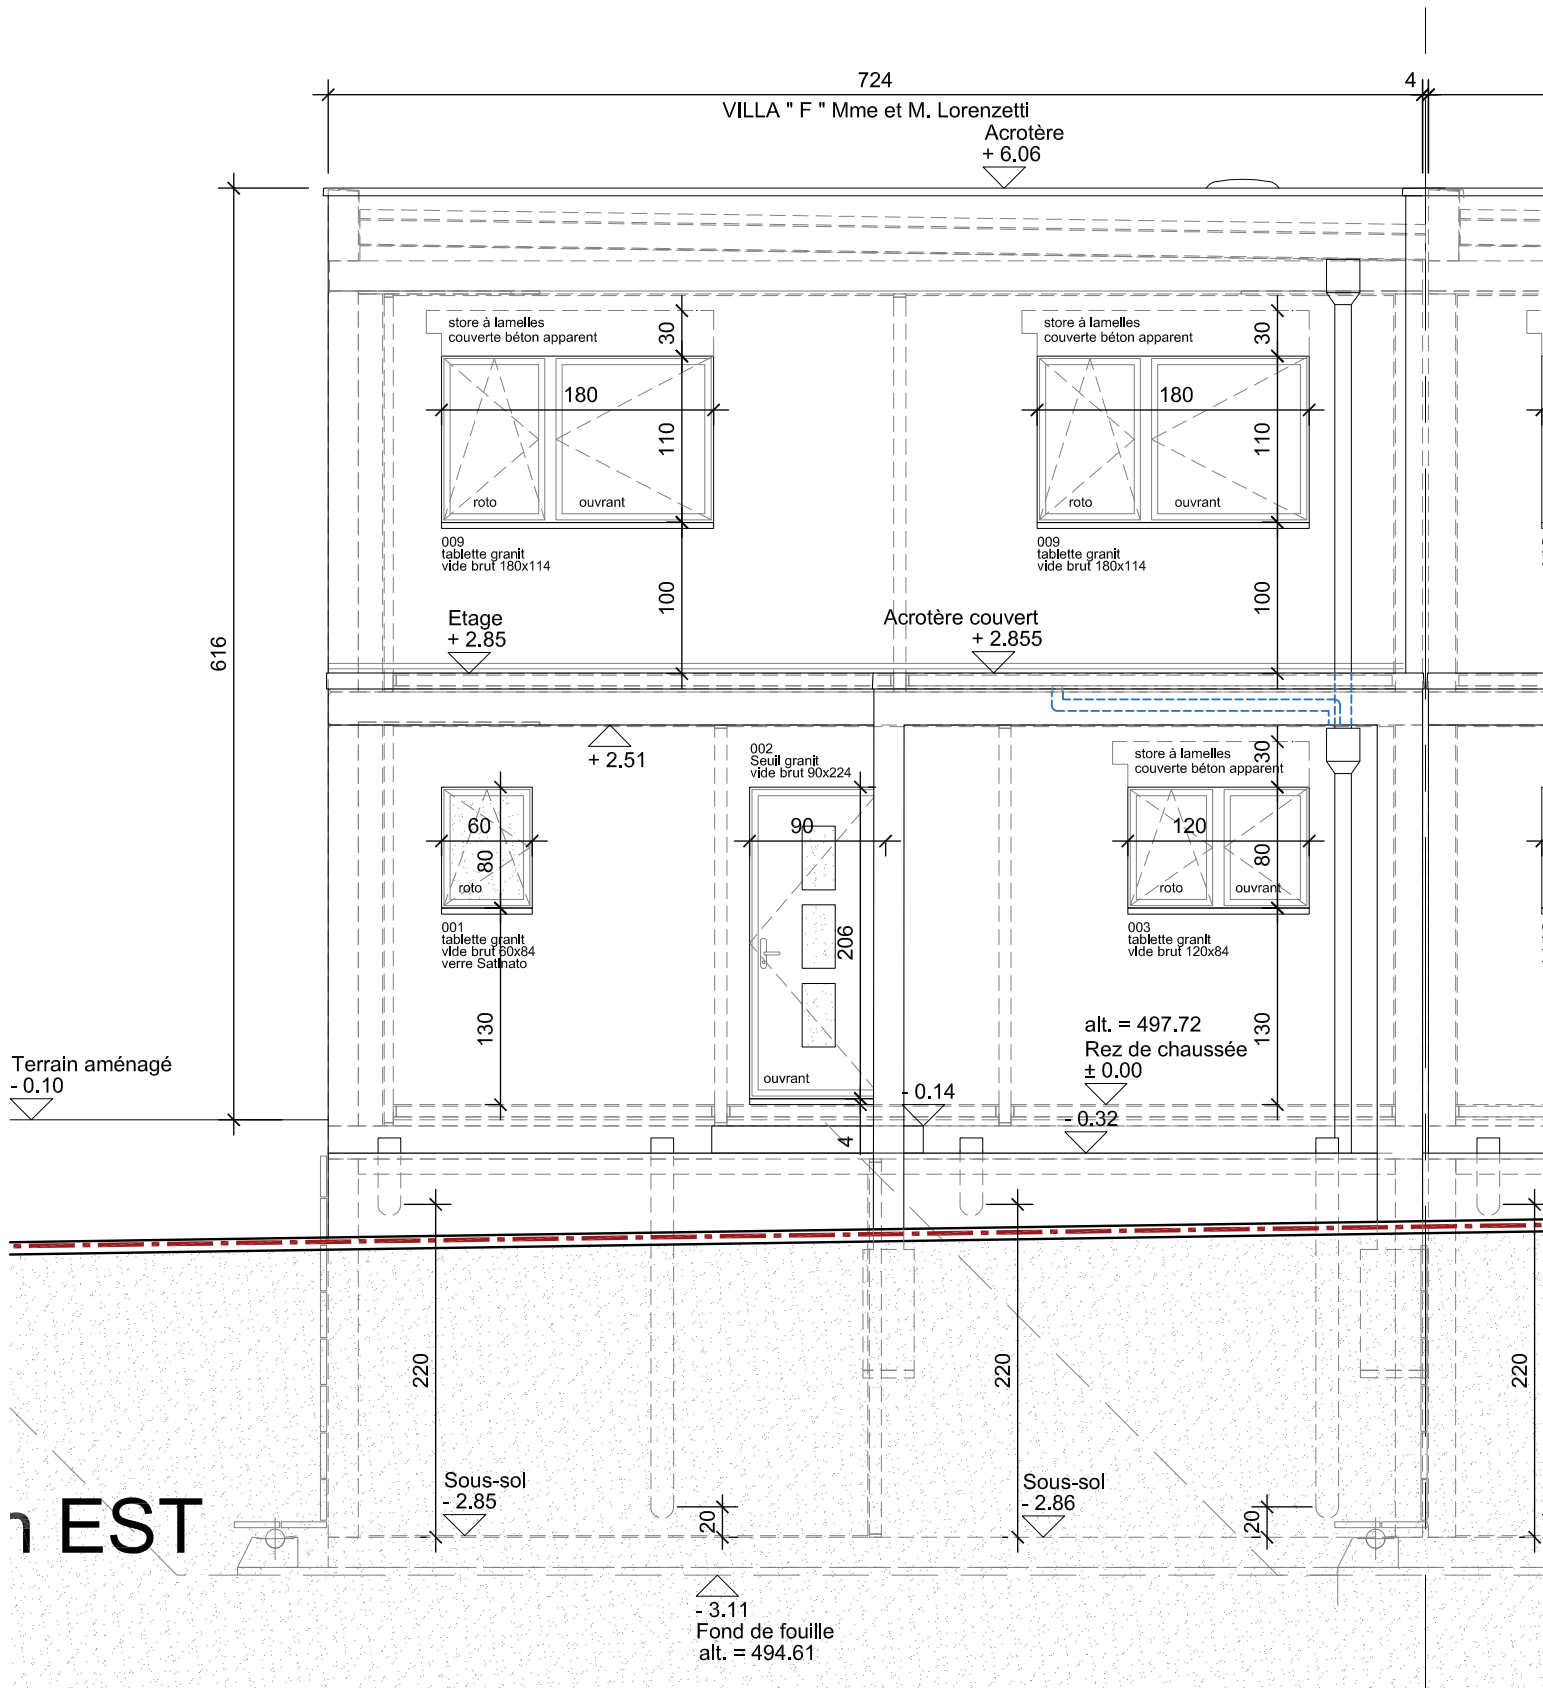

ELEVATION EST

Villa " F "

Mme. & M. LORENZETTI

"LACAPELA"

L'entrepreneur est tenu de contrôler
toutes les côtes et les niveaux sur les
plans ainsi que sur le chantier.

Les murs et les ouvertures
sont côtés finis

SOVALCO
Architecture & Construction

entreprise de construction générale
Tél. *4127 323 21 56
www.sovalco.ch info@sovalco.ch

Commune : UVRIER
Parcelle : 7819
Echelle : 1-50

DESSIN : cb
DATE D. : 05.03.2020
MODIF. : 19.08.2020

